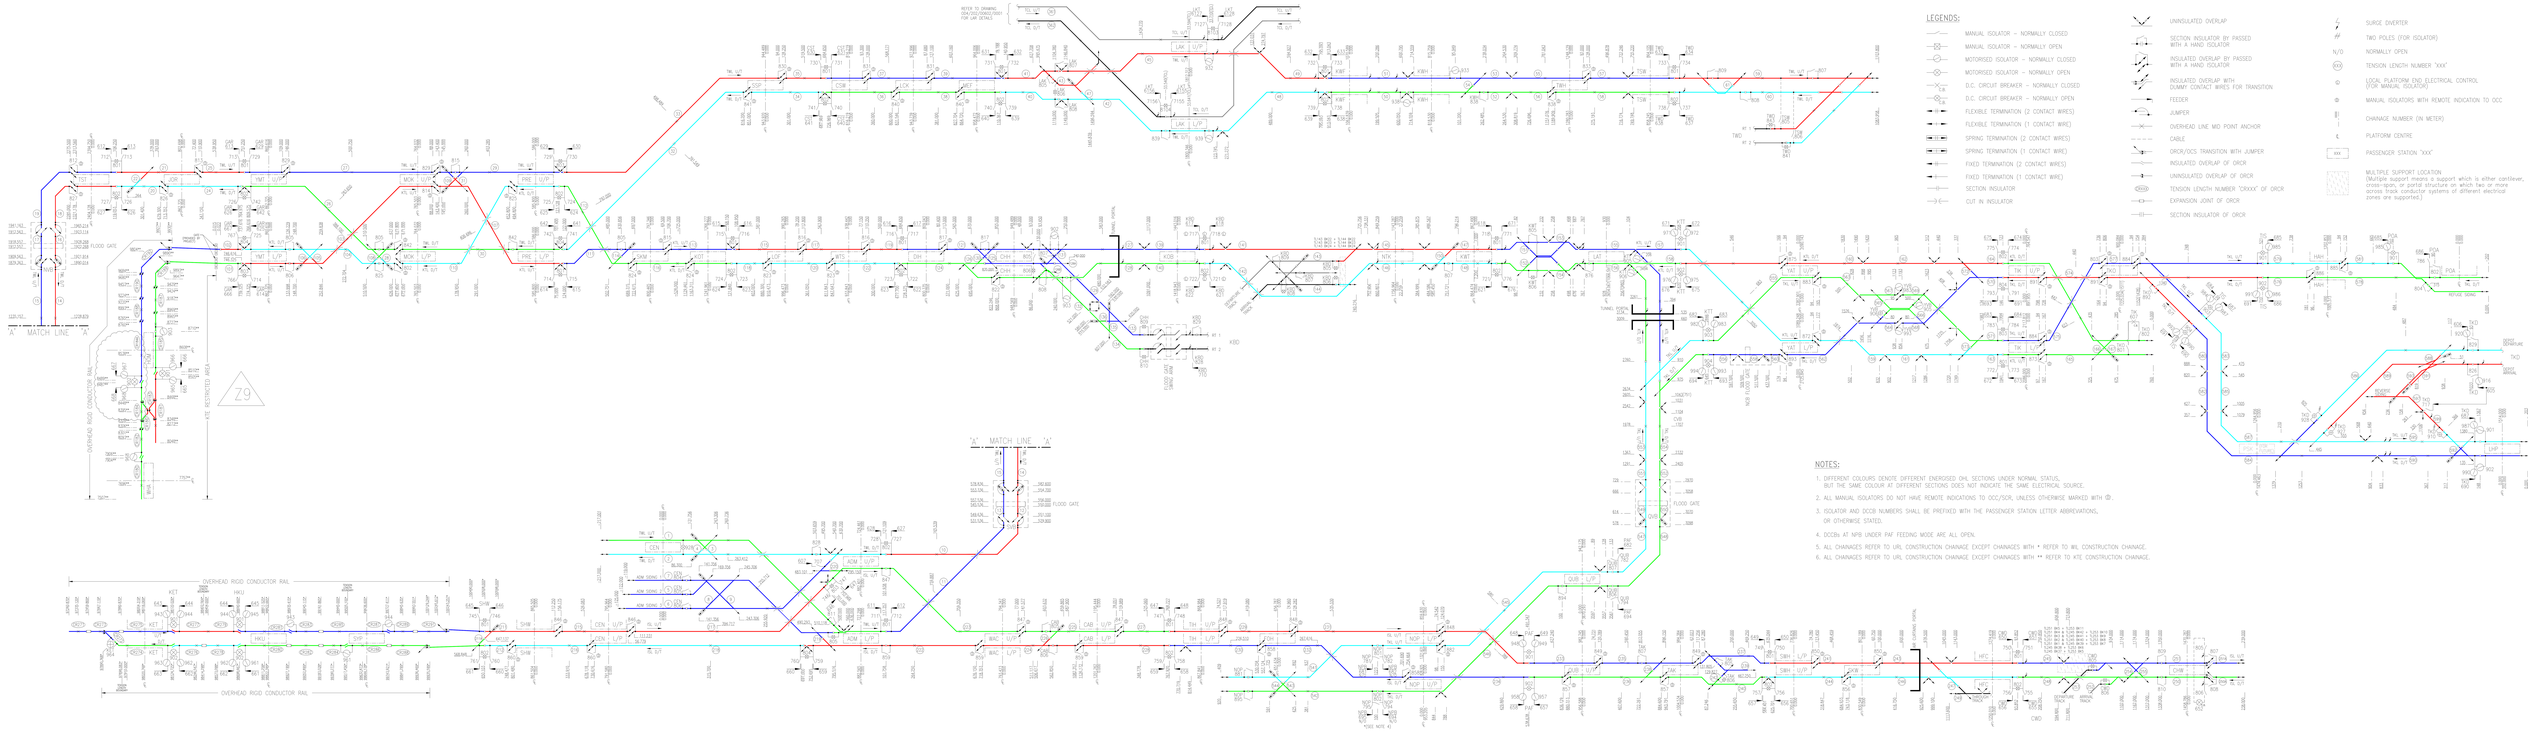

REV	DESCRIPTION	BY	DATE	APPROVED
Z9	SECTION INSULATOR ON CH-RARR ON SUPERSEDED BY INSULATED OVERLAP, TL CRYSTA SPLIT INTO TL DOYLES AND TL STRUBAL, NEW MID POINT ANCHOR ADDED ON CH-6395 ON.	CS C	25MAR16	A. CHAN
Z8	THE TEMPORARY SECTION INSULATOR AT CH-1000.022 YMT UP TRACK SIDING REMOVED AS PER EDDC NO. ZMT12810.	CS C	24MAR16	A. CHAN
X~Z7	REVISION DESCRIPTIONS SHALL REFER TO DRAWING RECORD IN DRAWING MANAGEMENT SYSTEM	---	---	---

DRAWN	K.H. PANG	A.D.
DESIGNED	---	---
CHECKED	PAUL LO	SM (O-PS)
APPROVED	S.C. CHOW	SEM (E&MS)
DATE	26/APR/1993	

ALL RIGHTS RESERVED
DO NOT SCALE DRAWINGS. ALL DIMENSIONS SHALL BE VERIFIED ON SITE.
© MTR CORPORATION LIMITED 2000. COPYRIGHT IN RESPECTS OF THIS DRAWING / DOCUMENT IS OWNED BY THE MTR CORPORATION LIMITED OF HONG KONG. NO REPRODUCTION OF THE DRAWING / DOCUMENT OR ANY PART OF WHATEVER BEARING IS PERMITTED WITHOUT THE PRIOR WRITTEN CONSENT OF THE MTR CORPORATION LIMITED.

MTR

ORIGINATOR
OPERATIONS DIVISION
TECHNICAL & ENGINEERING SERVICES DEPARTMENT

CADD REF. 0D4_202_00002_0001_Z9.dwg

TITLE
TRACTION - TENSION LENGTH FOR KTL, TWL, ISL & TKL

SCALE N.T.S.

DRAWING NO. 0D4/202/00002/0001

REV. Z9

Filename : D:\Users\TDMPS\Documents\ACAD\AT revised at SY\0D4_202_00002_0001_Z9.dwg
Date : 15/03/2016 13:51 Default : 1 Xref Name : 4x4.ctb Printed By : SY Amy Tai (MTR)
Printer : DWG To PDF.pc3